ARIA™
SIGNS & DESIGN
+Architectural Products

SIGN PACKAGE

Alexandria Design Lab

ALEXANDRIA

1955 MERIDIAN AVENUE, ANYTOWN, ST 00000

PROJECT INFO

QUANTITY : 1

SCOPE OF WORK :

FABRICATE AND INSTALL HALO-LIT REVERSE CHANNEL LETTERS: ALEXANDRIA DESIGN LAB

ARIA™ SIGNS & DESIGN +Architectural Products

PROJECT

PROJECT NAME :	ALEXANDRIA DESIGN LAB
LOCATION :	1955 MERIDIAN AVENUE
	ANYTOWN, ST 00000
DESCRIPTION :	EXTERIOR SIGNAGE
SALES REPS :	-
DESIGNER :	CLAUDE
DRAWING # :	261104.00
DATE :	11.04.2026

CLIENT

NAME :	ALEXANDRIA
TITLE :	-
PHONE :	-
EMAIL :	-
ADDRESS :	1955 MERIDIAN AVENUE
	ANYTOWN, ST 00000

REVISIONS

1	DATE :	-	BY :	-
2	DATE :	-	BY :	-
3	DATE :	-	BY :	-

COPYRIGHT

THIS IS AN ORIGINAL UNPUBLISHED DRAWING WHICH THE SOLE AND EXCLUSIVE PROPERTY OF ARIA SIGNS & DESIGN AND IS PROTECTED UNDER THE COPYRIGHT LAWS OF THE UNITED STATES OF AMERICA. IT WAS CREATED IN CONJUNCTION WITH A PROJECT PROPOSED BY ARIA SIGNS & DESIGN. IT IS NOT TO BE REPRODUCED, DUPLICATED, SHOWN, EXHIBITED, OR PHYSICALLY RE-CREATED IN WHOLE OR IN PART BY INDIVIDUAL, GROUP, ORGANIZATION OR ENTITY WITHOUT THE WRITTEN PERMISSION OF AN OFFICER OF ARIA SIGNS & DESIGN.

APPROVAL

THIS PROOF DRAWING IS FOR CUSTOMER OF ARIA SIGNS TO REVIEW AND APPROVAL BEFORE FABRICATION BEGINS. ARIA SIGNS WILL NOT BE RESPONSIBLE FOR PROBLEMS OR DISCREPANCIES THAT COULD HAVE BEEN REASONABLY PREVENTED BY THE PROPER REVIEW OF THIS DOCUMENT.

SKETCH MAY VARY FROM SPECIFIED COLORS. PHOTOS AND RENDERINGS ARE FOR VISUAL REFERENCE ONLY.

CUSTOMER PROVIDES DEDICATED 120 VOLT SIGN CIRCUITS WITH A GROUND WIRE TO BE PROVIDED WITHIN 4' OF THE SIGN(S) BEFORE THE INSTALLATION DATE.

THE CUSTOMER SHALL PROVIDE ACCESSIBILITY TO BUILDING IF IT WAS NEEDED FOR INSTALLATION OR FOR INSPECTION OR SERVICE.

SIGN-OFF

COMMENTS :

SIGNATURE

DATE

PRINTED NAME

TITLE

DAY RENDER QUANTITY : 1

SCOPE OF WORK :

FABRICATE AND INSTALL HALO-LIT REVERSE CHANNEL LETTERS: ALEXANDRIA DESIGN LAB

ARIA™
SIGNS & DESIGN
+Architectural Products



PROPOSED SIGNAGE

SCALED PROPORTIONALLY

ARIA™
SIGNS & DESIGN
+Architectural Products

NIGHT RENDER — QUANTITY : 1

SCOPE OF WORK :

FABRICATE AND INSTALL HALO-LIT REVERSE CHANNEL LETTERS: ALEXANDRIA DESIGN LAB



PROPOSED SIGNAGE


SCALED PROPORTIONALLY

ARIA™
SIGNS & DESIGN
+Architectural Products

SIGN LOCATION — QUANTITY : 1

SCOPE OF WORK :

FABRICATE AND INSTALL HALO-LIT REVERSE CHANNEL LETTERS: ALEXANDRIA DESIGN LAB

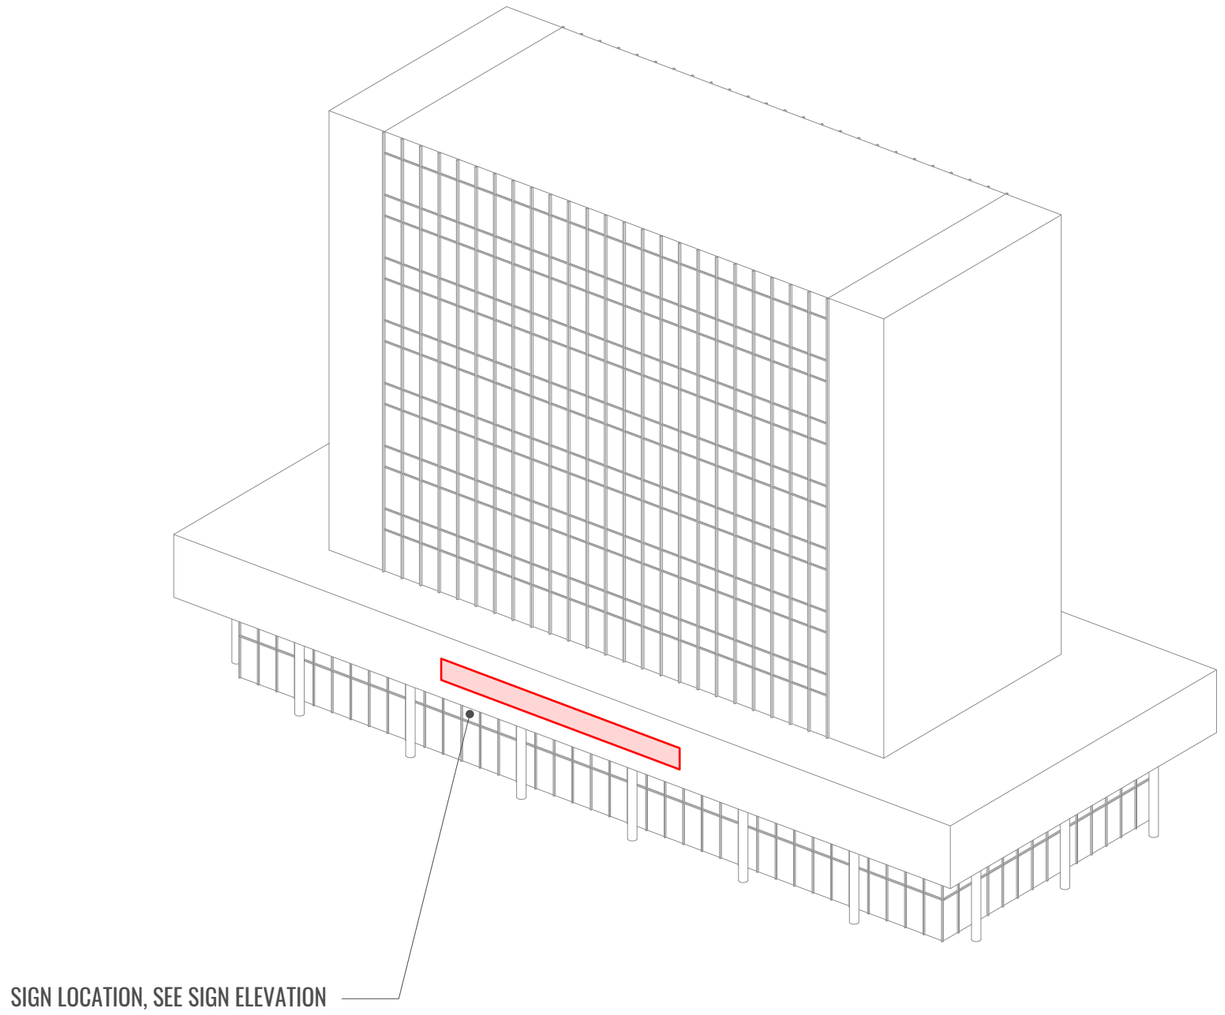

SIGN LOCATION


AXONOMETRIC, 1/32" = 1'-0"

ARIN™ SIGNS & DESIGN +Architectural Products

BUILDING PLAN — QUANTITY : 1

SCOPE OF WORK :

FABRICATE AND INSTALL HALO-LIT REVERSE CHANNEL LETTERS: ALEXANDRIA DESIGN LAB

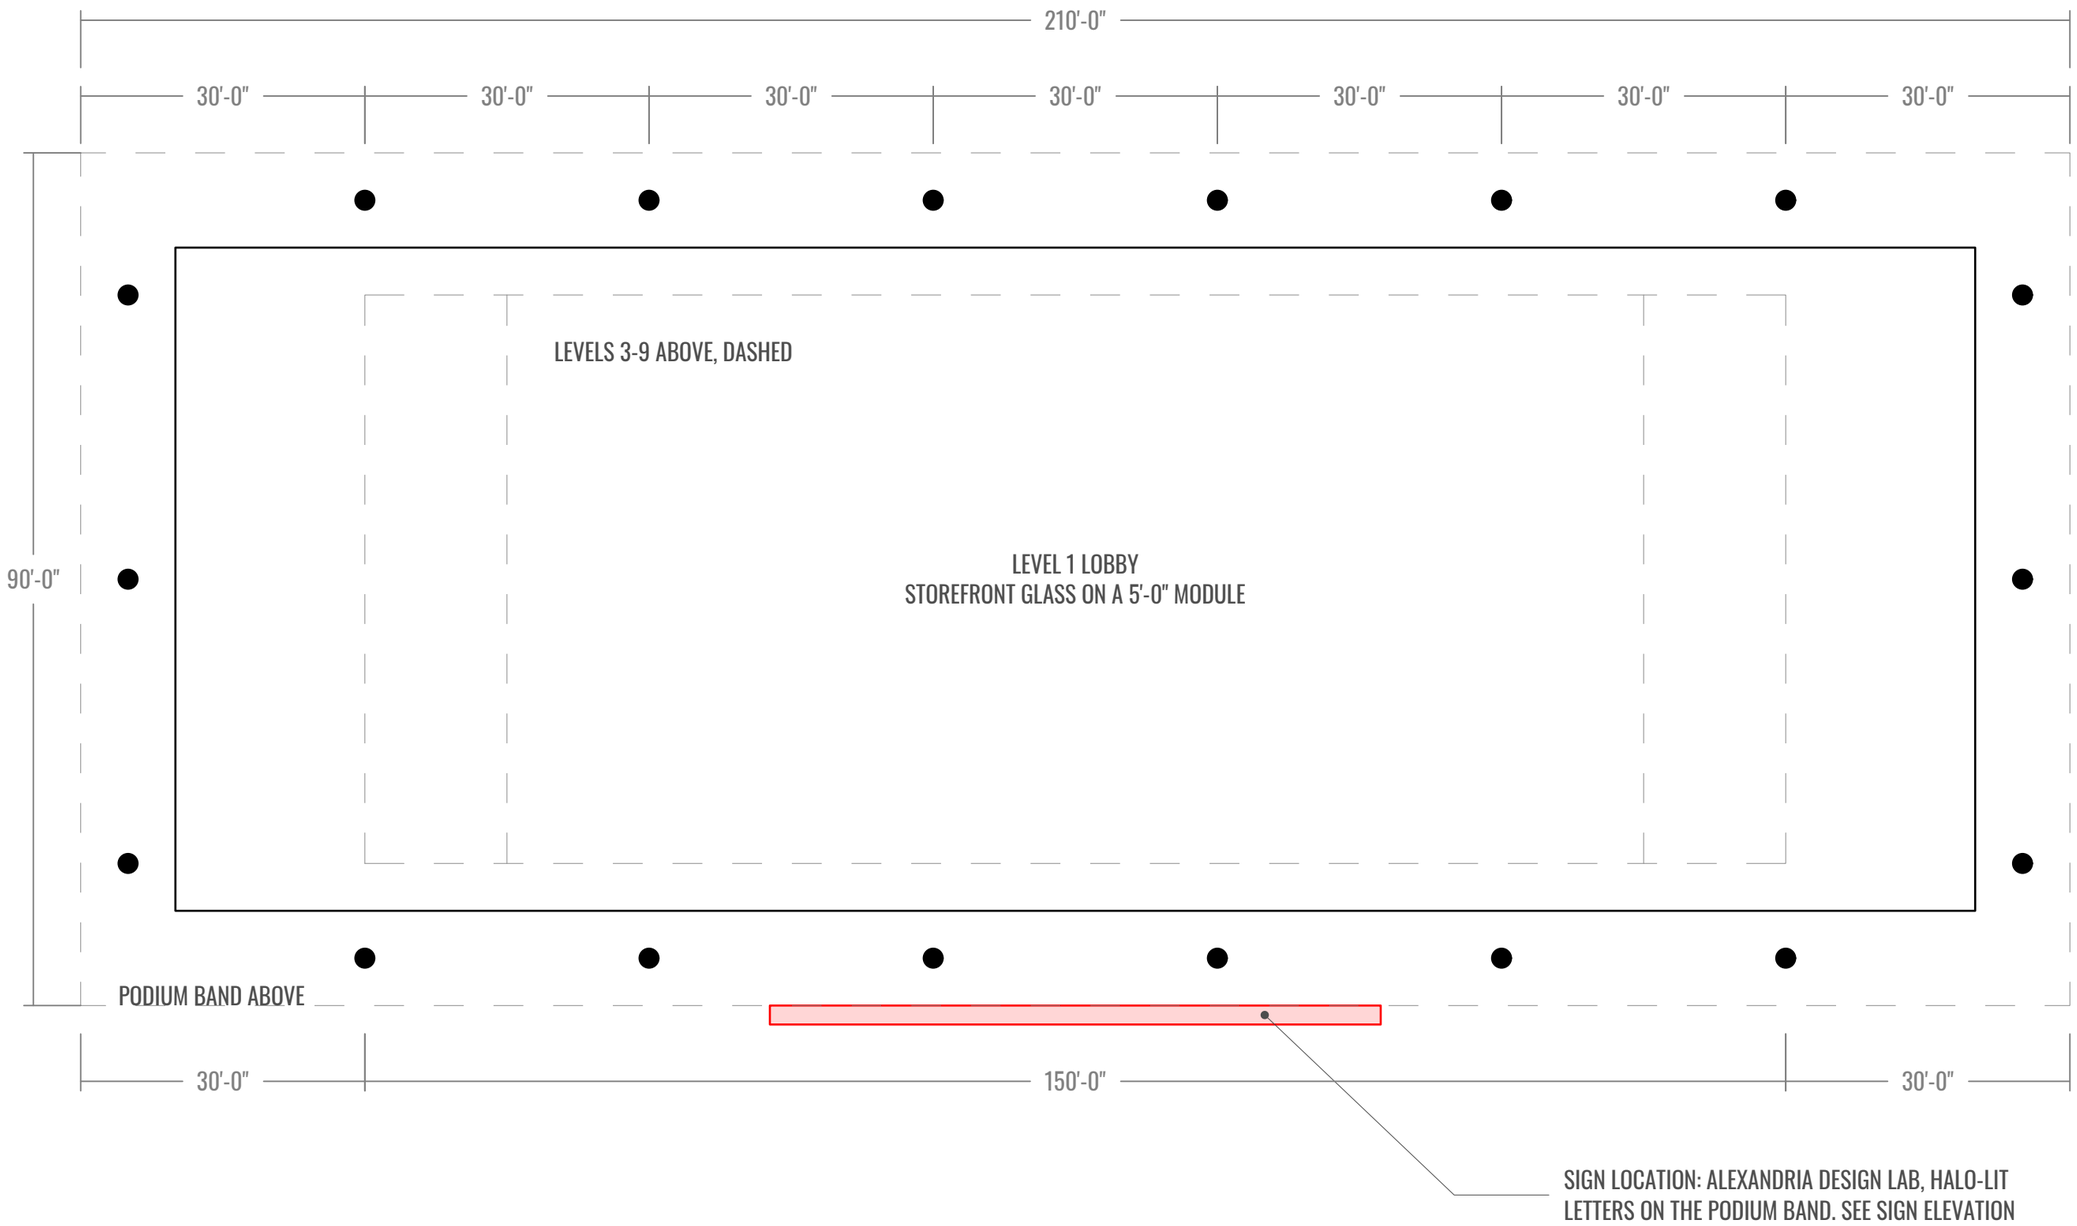

GROUND FLOOR PLAN

1/16" = 1'-0"


BUILDING ELEVATIONS — QUANTITY : 1

SCOPE OF WORK :


FABRICATE AND INSTALL HALO-LIT REVERSE CHANNEL LETTERS: ALEXANDRIA DESIGN LAB

ARIN™ SIGNS & DESIGN +Architectural Products

LEVELS 3-9: 15'-0" FLOOR TO FLOOR,
10'-0" VISION GLASS UNDER A 5'-0" SPANDREL,
MULLIONS AT 5'-0". PRECAST END BAYS AND BAND.

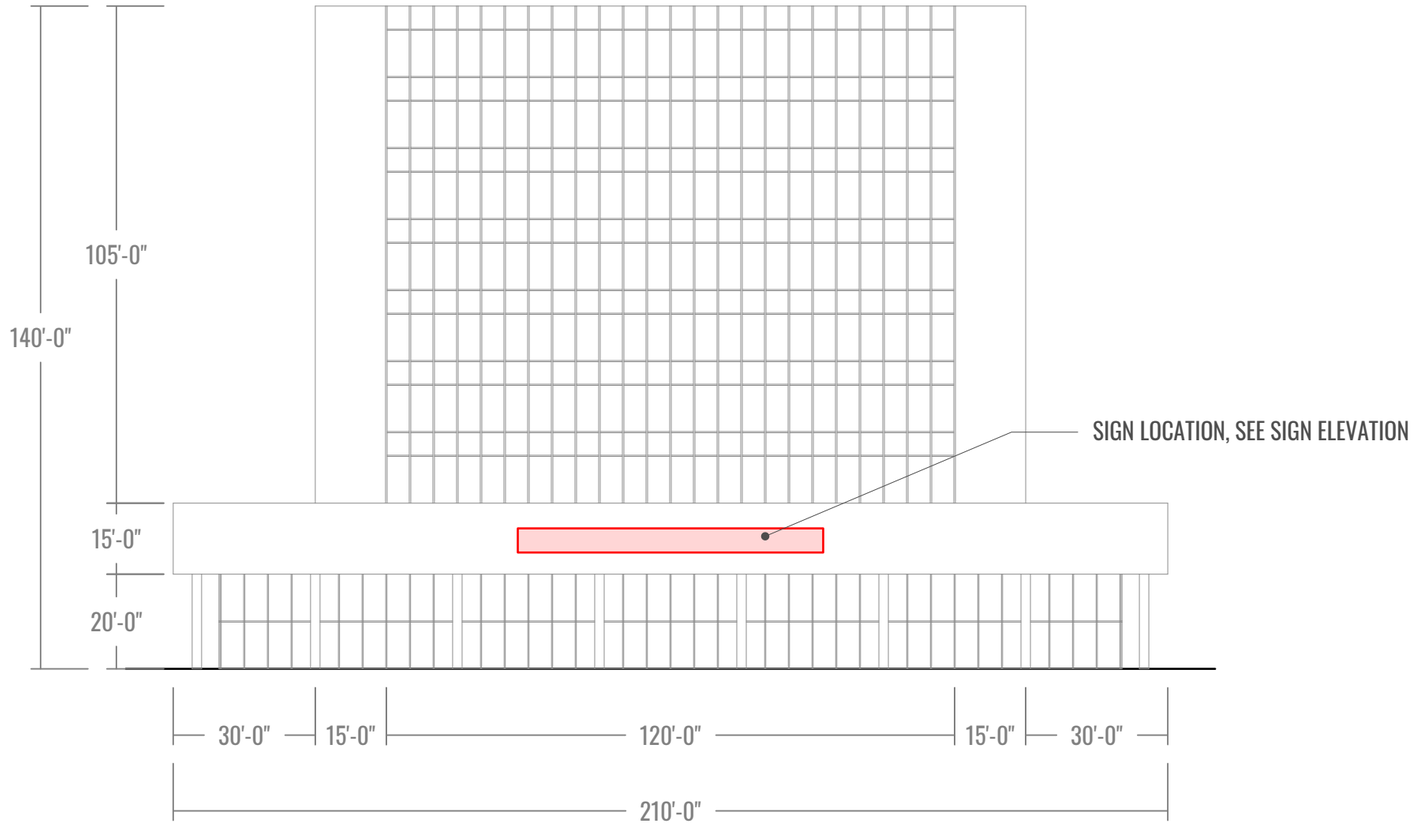

FRONT ELEVATION
1/32" = 1'-0"

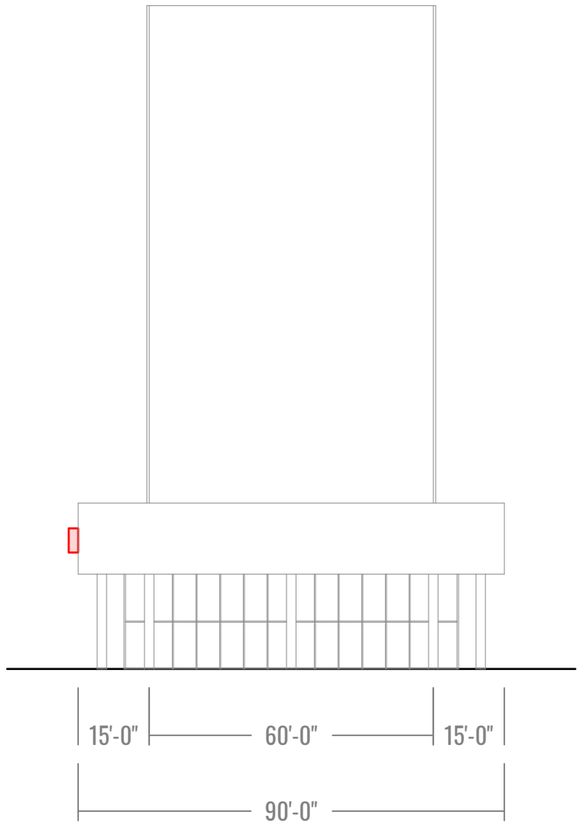


EAST ELEVATION
1/32" = 1'-0"

ARIA™ SIGNS & DESIGN +Architectural Products

SIGN ELEVATION — QUANTITY : 1

SCOPE OF WORK :

FABRICATE AND INSTALL HALO-LIT REVERSE CHANNEL LETTERS: ALEXANDRIA DESIGN LAB

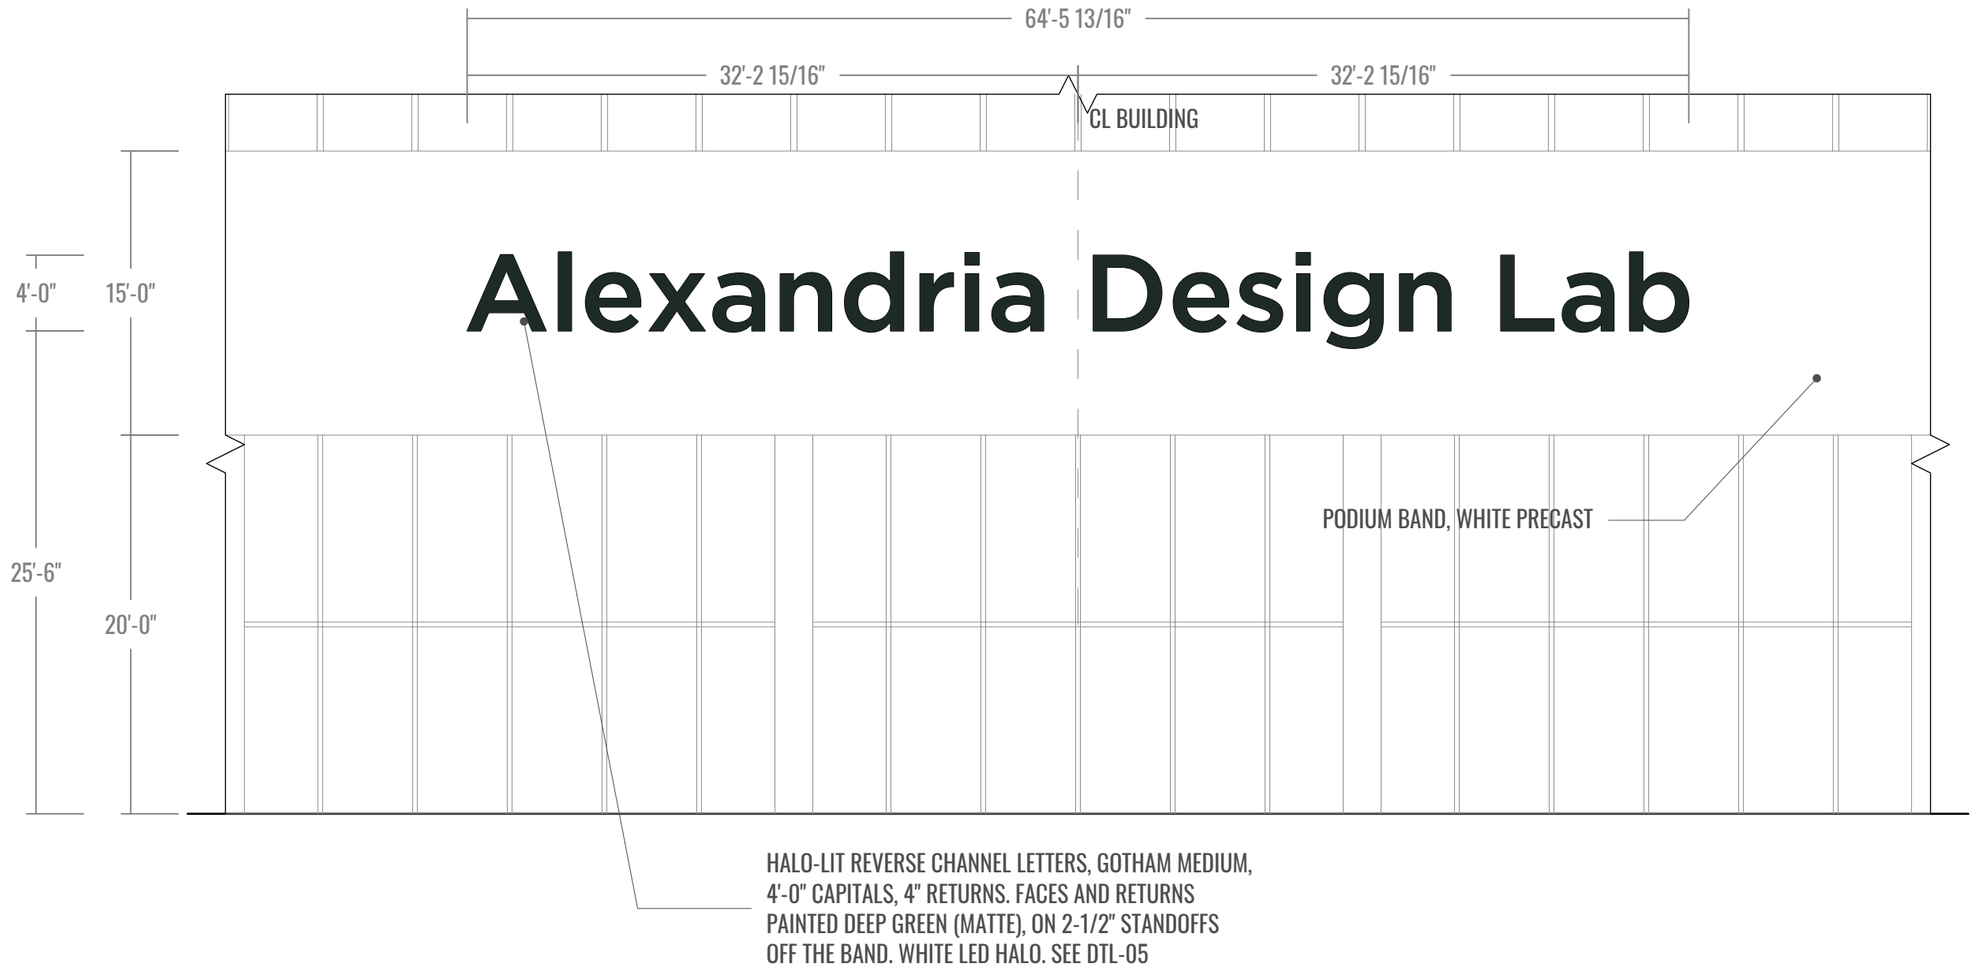


SIGN ELEVATION

1/8" = 1'-0"

SIGN DETAILS — QUANTITY : 1

SCOPE OF WORK :

FABRICATE AND INSTALL HALO-LIT REVERSE CHANNEL LETTERS: ALEXANDRIA DESIGN LAB

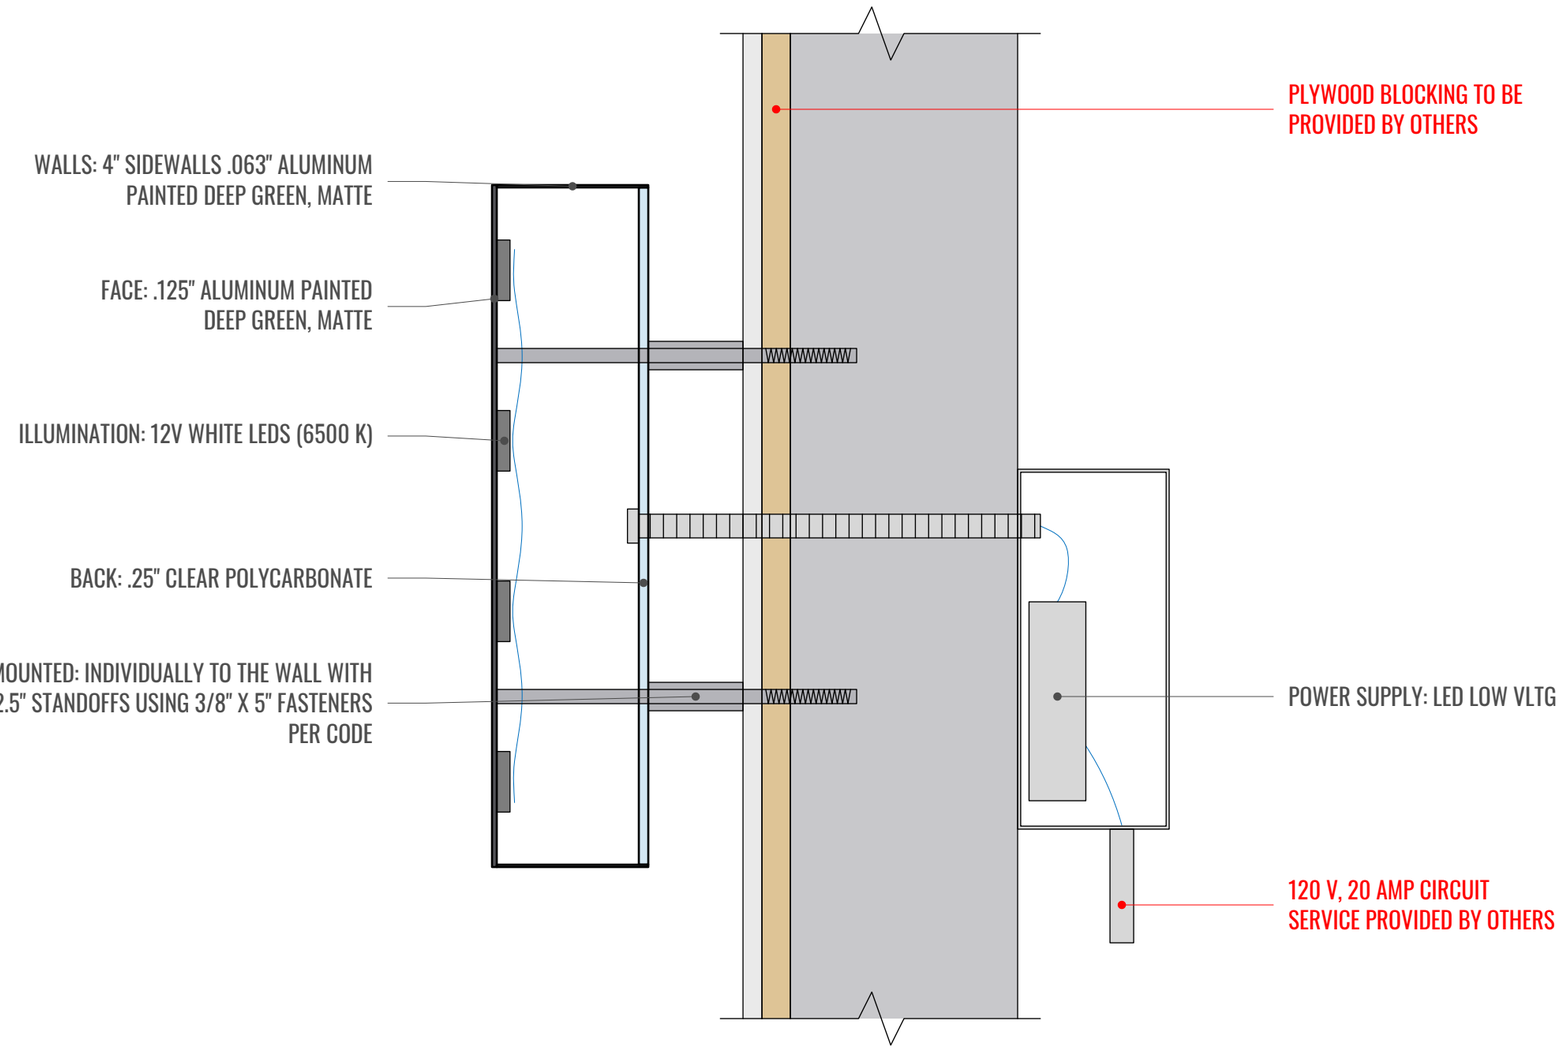

DTL-05 ILLUMINATED REVERSE CHANNEL LETTERS STANDOFF MOUNT (HALO-LIT)

LETTER MOUNTING DETAIL

3" = 1'-0"

COLORS, MATERIALS & FINISHES — QUANTITY : 1

SCOPE OF WORK :

FABRICATE AND INSTALL HALO-LIT REVERSE CHANNEL LETTERS: ALEXANDRIA DESIGN LAB

PAINT



P1 DEEP GREEN

MATTHEWS PAINT, CUSTOM MATCH TO RGB 30-42-36

FINISH : MATTE — USED ON : LETTER FACES AND RETURNS


MATERIALS



M1 ALUMINUM

.125" FACES AND .063" X 4" RETURNS

FINISH : PAINTED P1 — USED ON : LETTERS

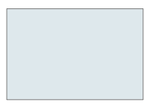

M2 CLEAR POLYCARBONATE

.25" CLEAR POLYCARBONATE

USED ON : LETTER BACKS



M3 STANDOFFS

2-1/2" ALUMINUM STANDOFFS, 3/8" X 5" FASTENERS PER CODE

FINISH : CLEAR ANODIZED — USED ON : LETTER MOUNTING

ELECTRICAL

E1 ILLUMINATION

12V WHITE LED MODULES, 6500 K

USED ON : INSIDE EACH LETTER

E2 POWER SUPPLY

LED LOW VOLTAGE, REMOTE BEHIND THE BAND

USED ON : PODIUM BAND

E3 SERVICE

ONE DEDICATED 120 V, 20 A CIRCUIT, BY OTHERS

USED ON : WITHIN 4' OF THE SIGN